
HOUSE WIRING LAYOUT — PLAN VIEW

Student No: _____ | Scale 1:100 | SANS 10142-1 Compliant | Date: 2026

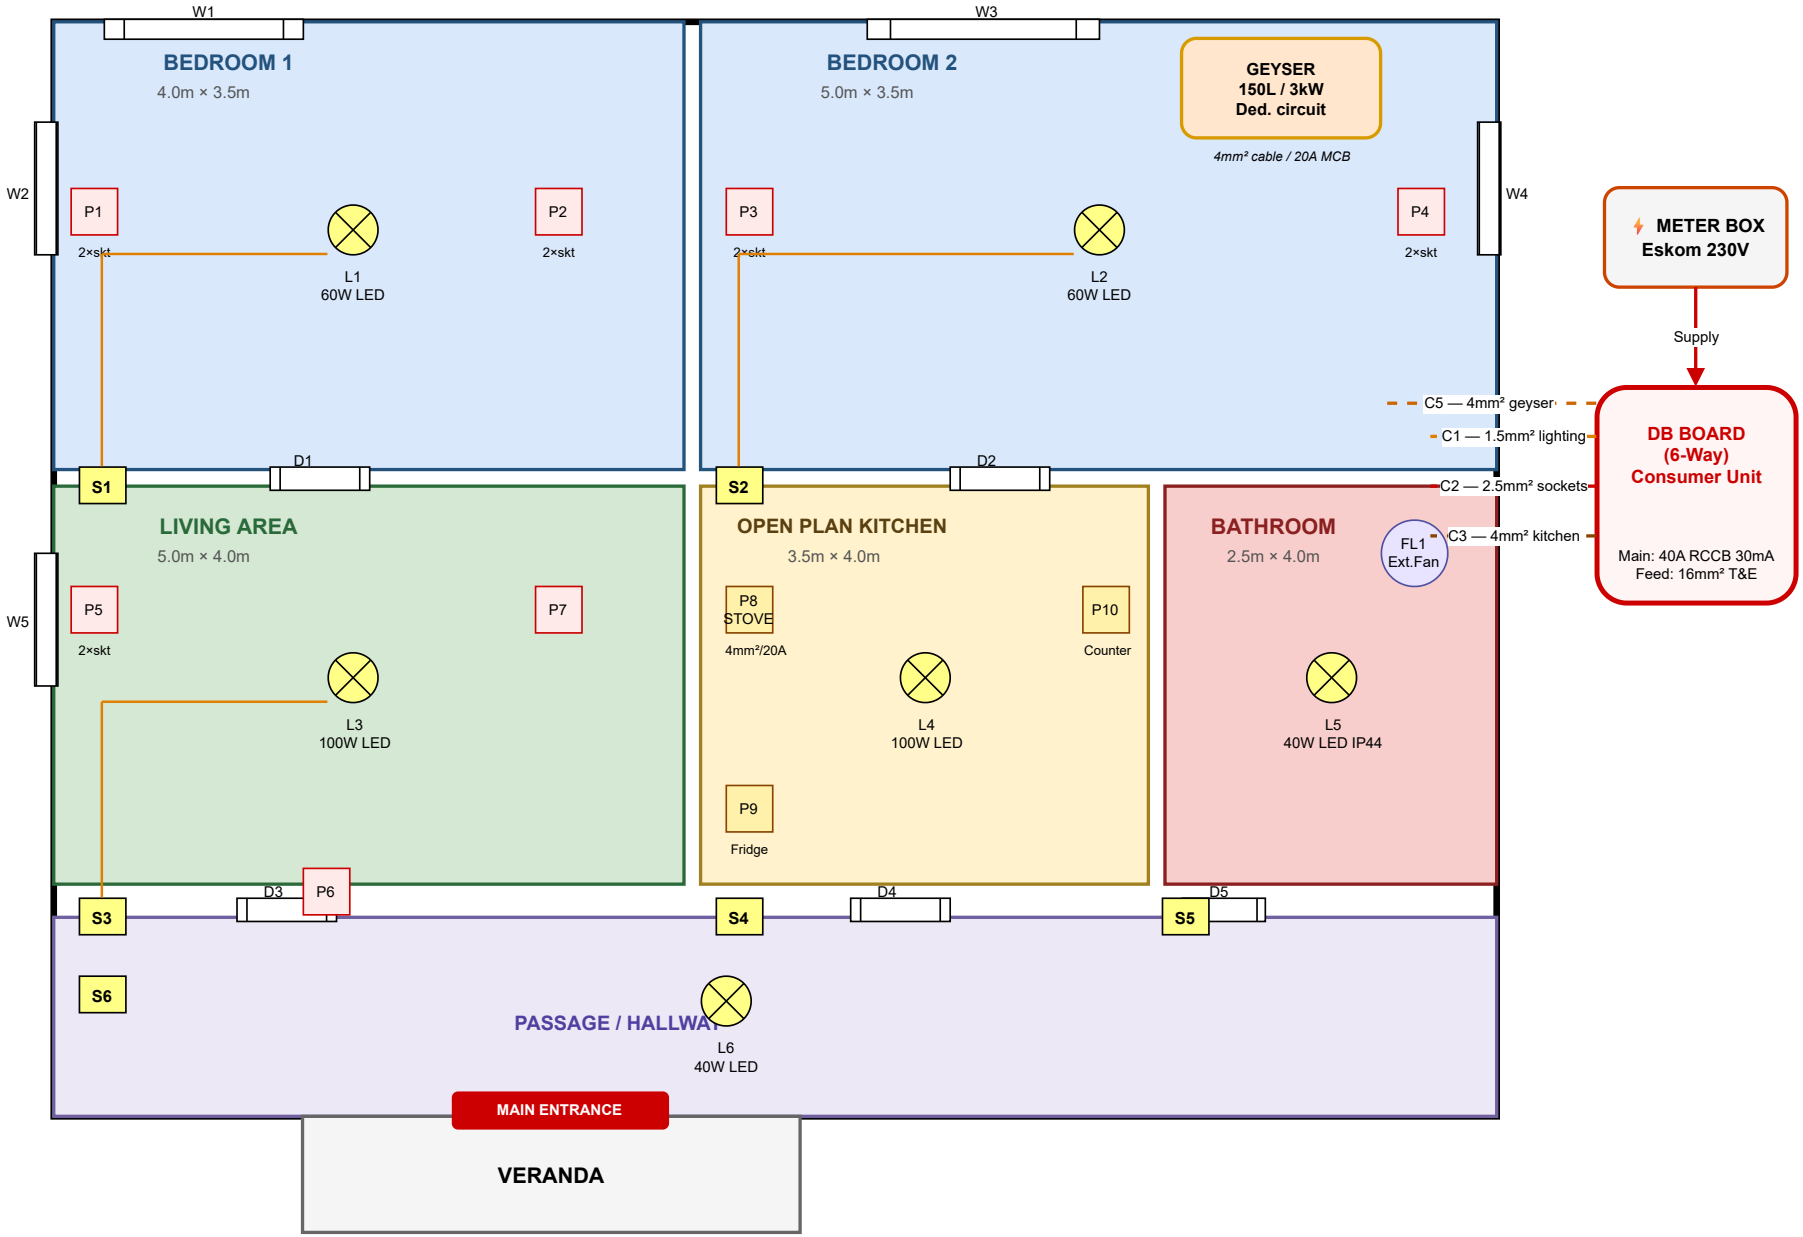

LEGEND / SYMBOL KEY

- Ceiling light (Ln)
- S — Light switch (Sn)
- Socket outlet (Pn)
- Extractor fan (FLn)
- DB Distribution board
- Lighting circuit C1 (1.5mm²)
- Socket circuit C2 (2.5mm²)
- Kitchen/Geyser C3–C5 (4mm²)

All wiring per SANS 10142-1 | Wire colors: Brown=Live, Blue=Neutral, Green/Yellow=Earth | Heights: sockets 300mm AFF, switches 1400mm AFF