
HOUSE WIRING LAYOUT — PLAN VIEW

Student No: _____ | Scale 1:100 | SANS 10142-1 | Date: 2026

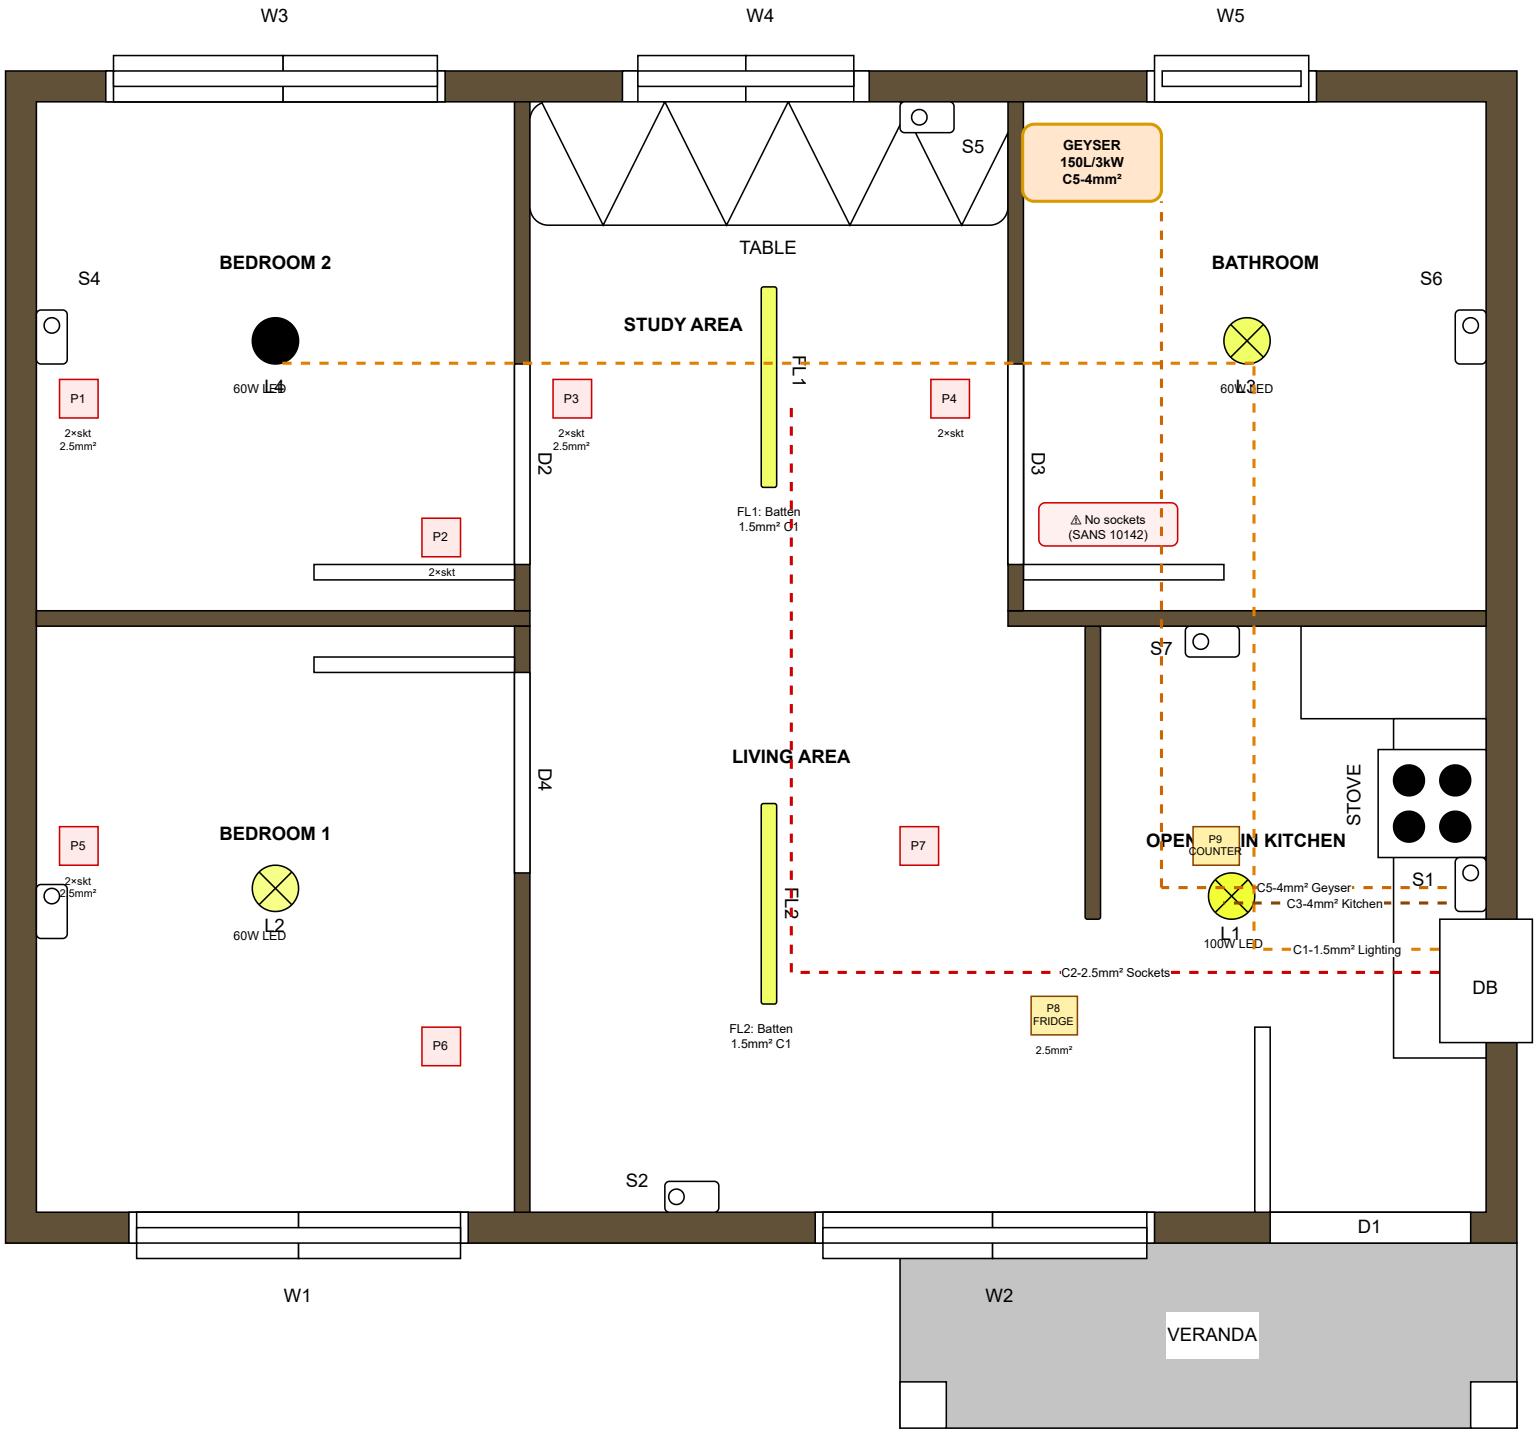

LEGEND / SYMBOL KEY

- Ceiling light (Ln)
- S — Light switch (Sn)
- P — Socket outlet (Pn)
- FL — Fluorescent/Batten light
- DB — Distribution Board
- W — Window | D — Door
- C1 Lighting 1.5mm²
- C2 Sockets 2.5mm²
- C3 Kitchen 4mm²
- C5 Geyser 4mm²

All wiring per SANS 10142-1 | Brown=Live | Blue=Neutral | Green/Yellow=Earth | Sockets at 300mm AFF | Switches at 1400mm AFF