
HOUSE WIRING LAYOUT — FLOOR PLAN VIEW

Student No: **224473710** | Scale 1:100 | SANS 10142-1 | Date: 30 March 2026

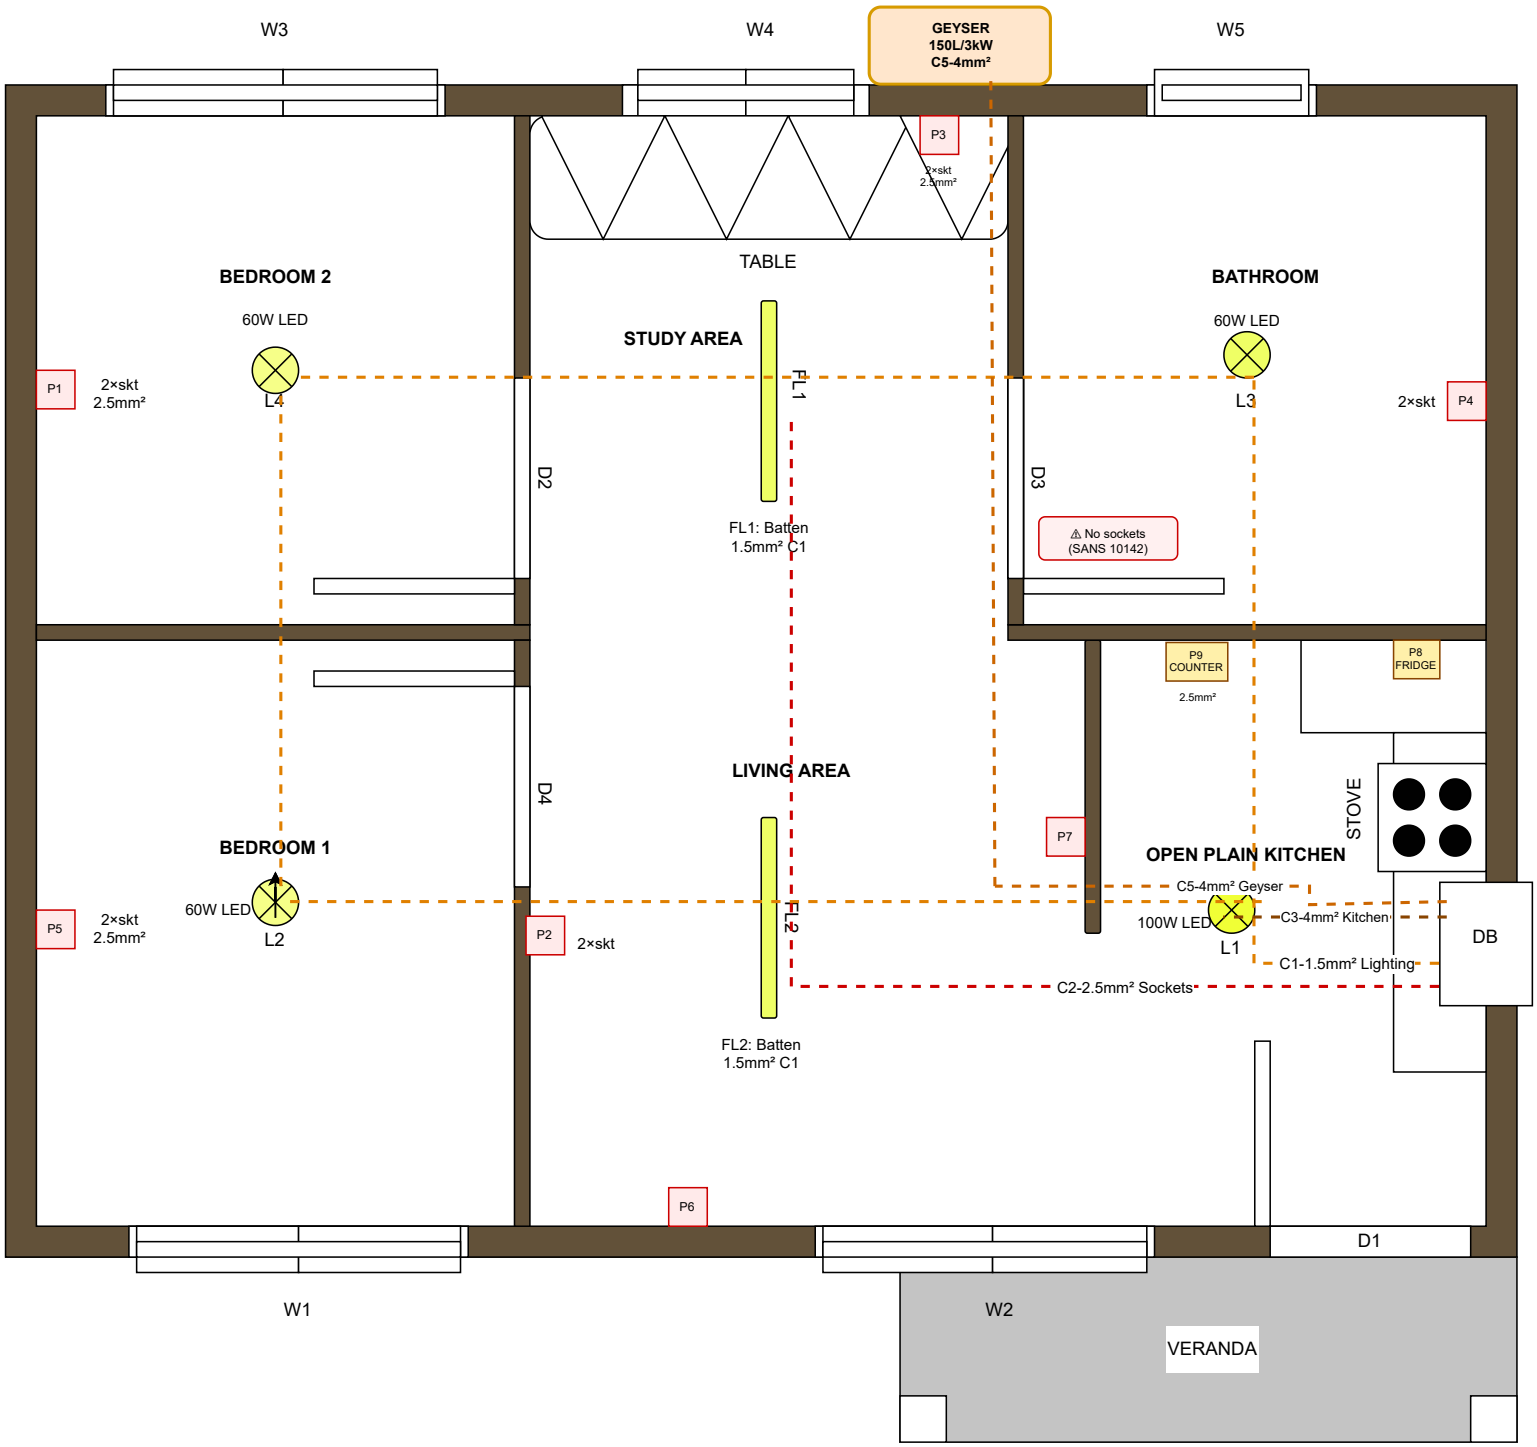

SYMBOL KEY

Ceiling light (Ln) | S Light switch (Sn) | P Socket outlet (Pn) | FL — Fluorescent/Batten light | DB — Distribution Board | W — Window | D — Door

C1 Lighting 1.5mm² | C2 Sockets 2.5mm² | C3 Kitchen 4mm² | C5 Geyser 4mm²

All wiring per SANS 10142-1 | Brown=Live | Blue=Neutral | Green/Yellow=Earth | Sockets at 300mm AFF | Switches at 1400mm AFF